


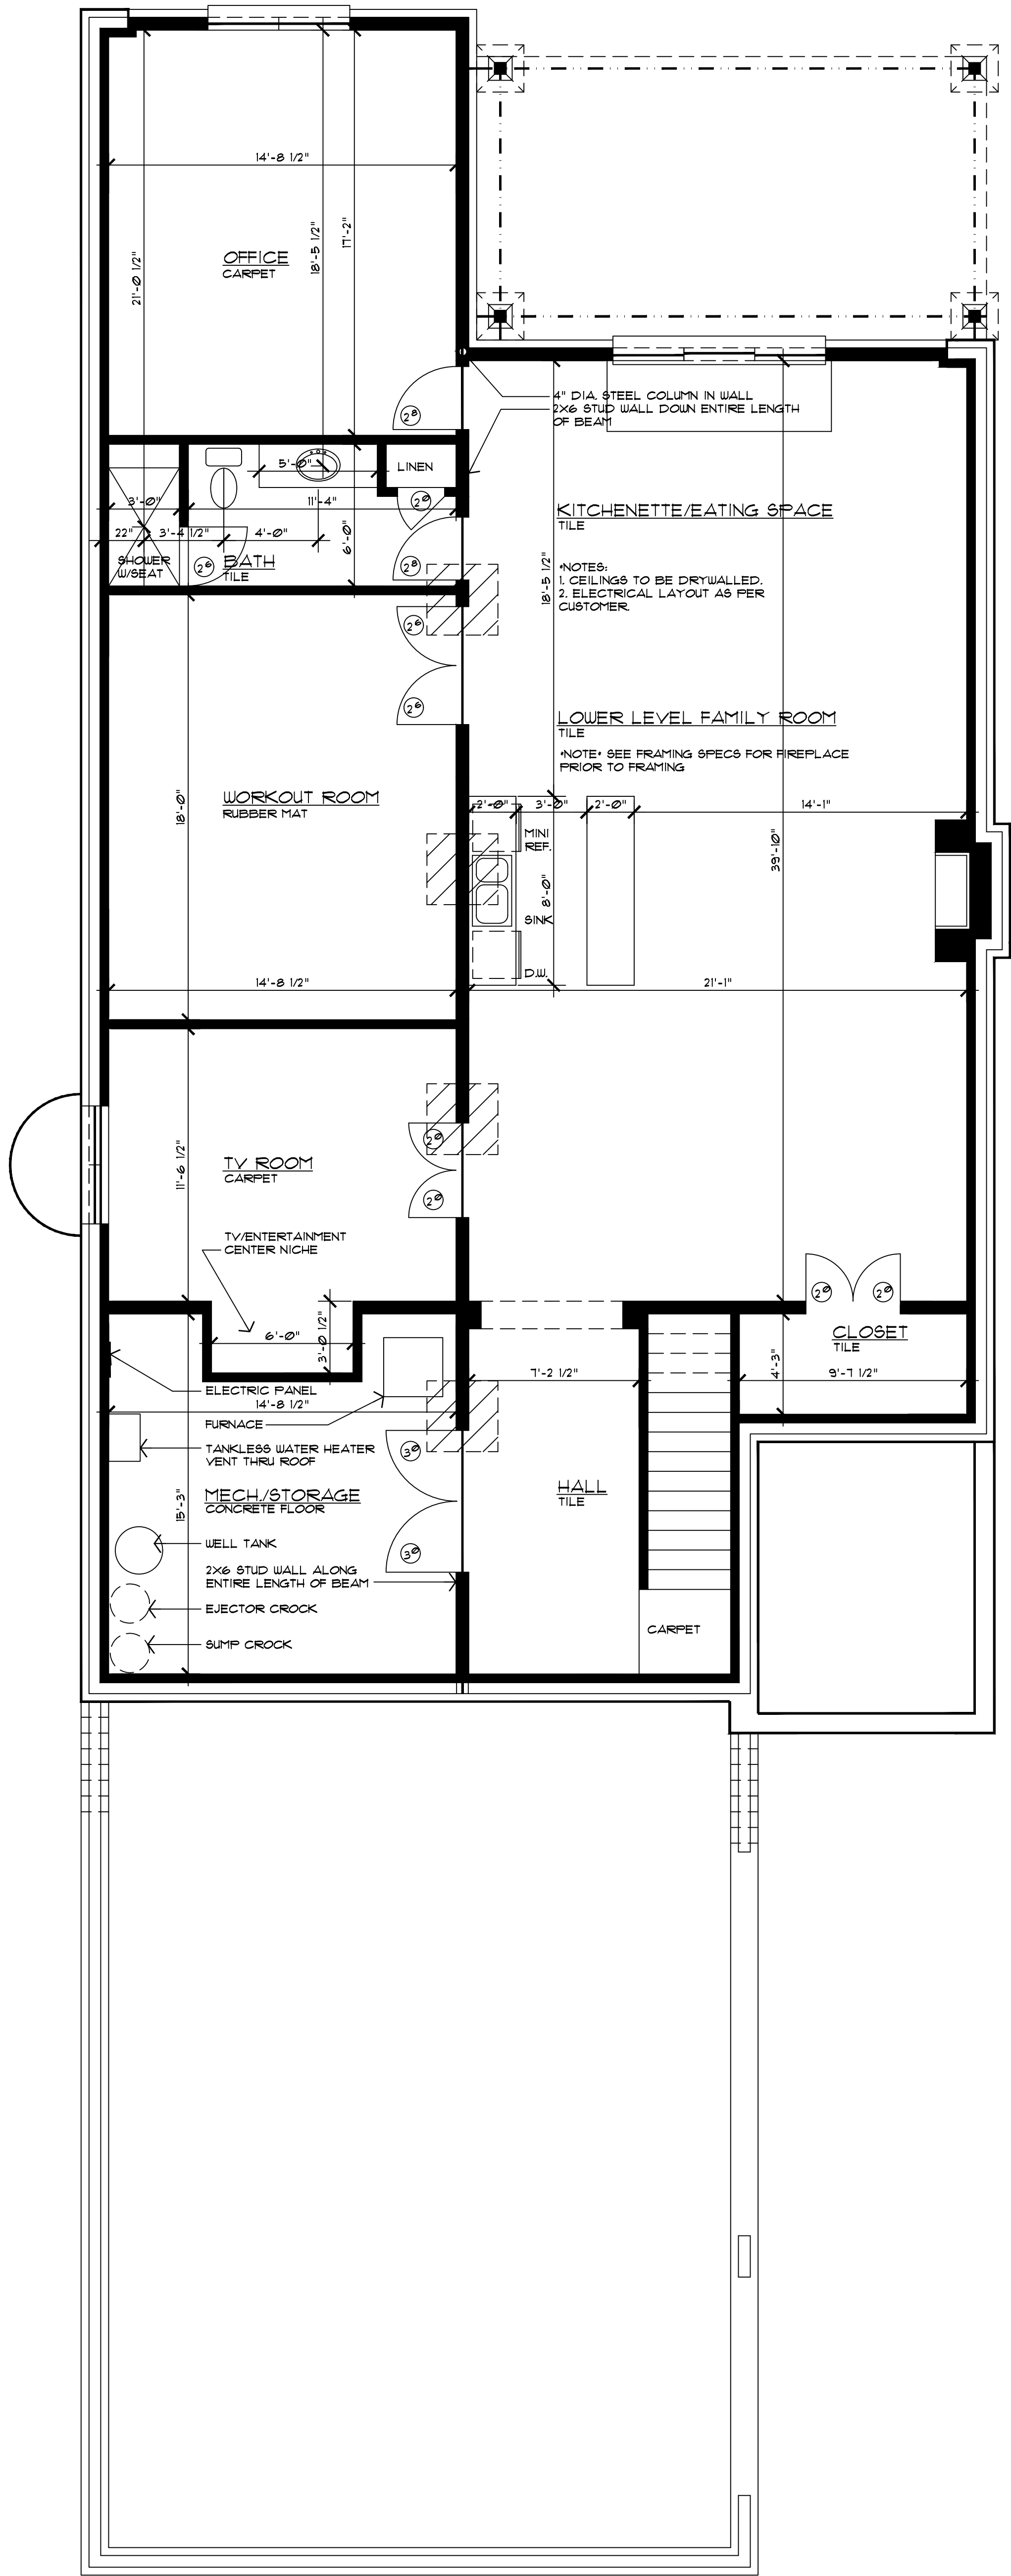

## FINISHED BASEMENT PLAN

2115 SQUARE FEET

SCALE: 1/4"=1'-0"

Designed By:

**Vild Design Group, Inc.**

A Home Plan Design Company  
Phone 248.755.6254  
Email: VildDesignGroup@yahoo.com

HOME PLAN PREPARED FOR:  
MATT DRESDEN

BUILDER:

### DRAWING DATES

- ☐ PRELIMINARY  
DATE: 06/27/2025  
☒ FINAL DRAWINGS  
DATE: 09/05/2025  
☐ PLOT PLAN  
DATE:

### REVISIONS

|  |  |
|--|--|
|  |  |
|  |  |
|  |  |
|  |  |
|  |  |
|  |  |
|  |  |

### DRAWING DESCRIPTION

- FINISHED BASEMENT PLAN  
●  
JOB #: 25-0905  
SHEET 2 OF 1