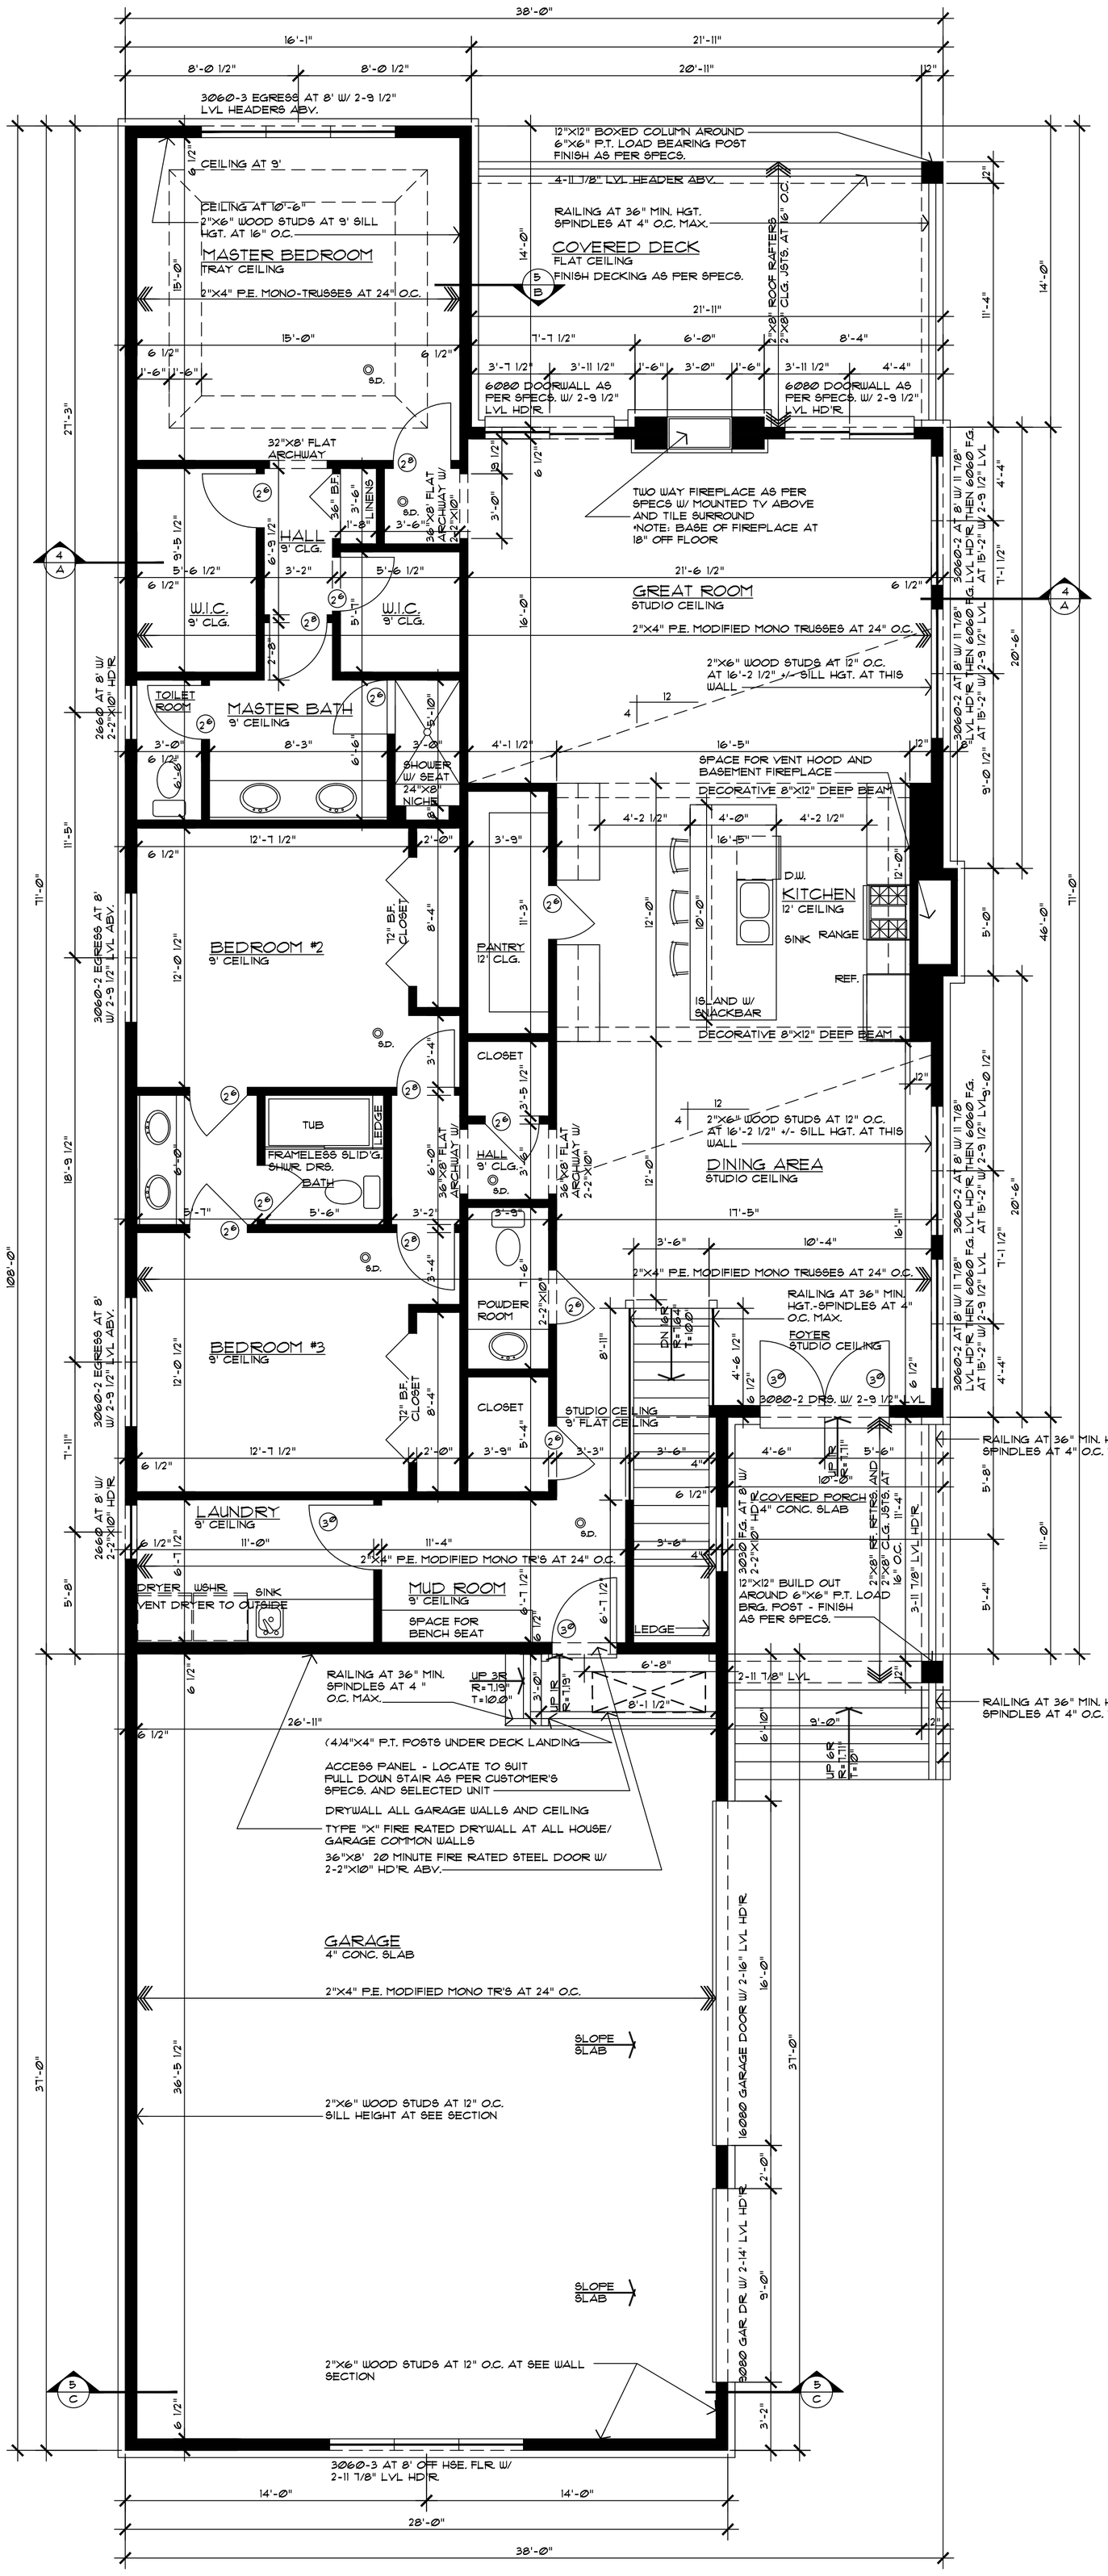


FLOOR PLAN

2281 SQUARE FEET TOTAL

SCALE: 1/4"=1'-0"

Designed By:

Vild Design Group, Inc.

A Home Plan Design Company
Phone 248.755.6254
Email: VildDesignGroup@yahoo.com

HOME PLAN PREPARED FOR:
MATT DRESDEN

BUILDER:

DRAWING DATES

- ☐ PRELIMINARY DATE:06/27/2025
- ■ FINAL DRAWINGS DATE: 09/05/2025
- ☐ PLOT PLAN DATE:

REVISIONS

DRAWING DESCRIPTION

- ● FLOOR PLAN
- ●

JOB #: 25-0905

SHEET 3 OF 7