


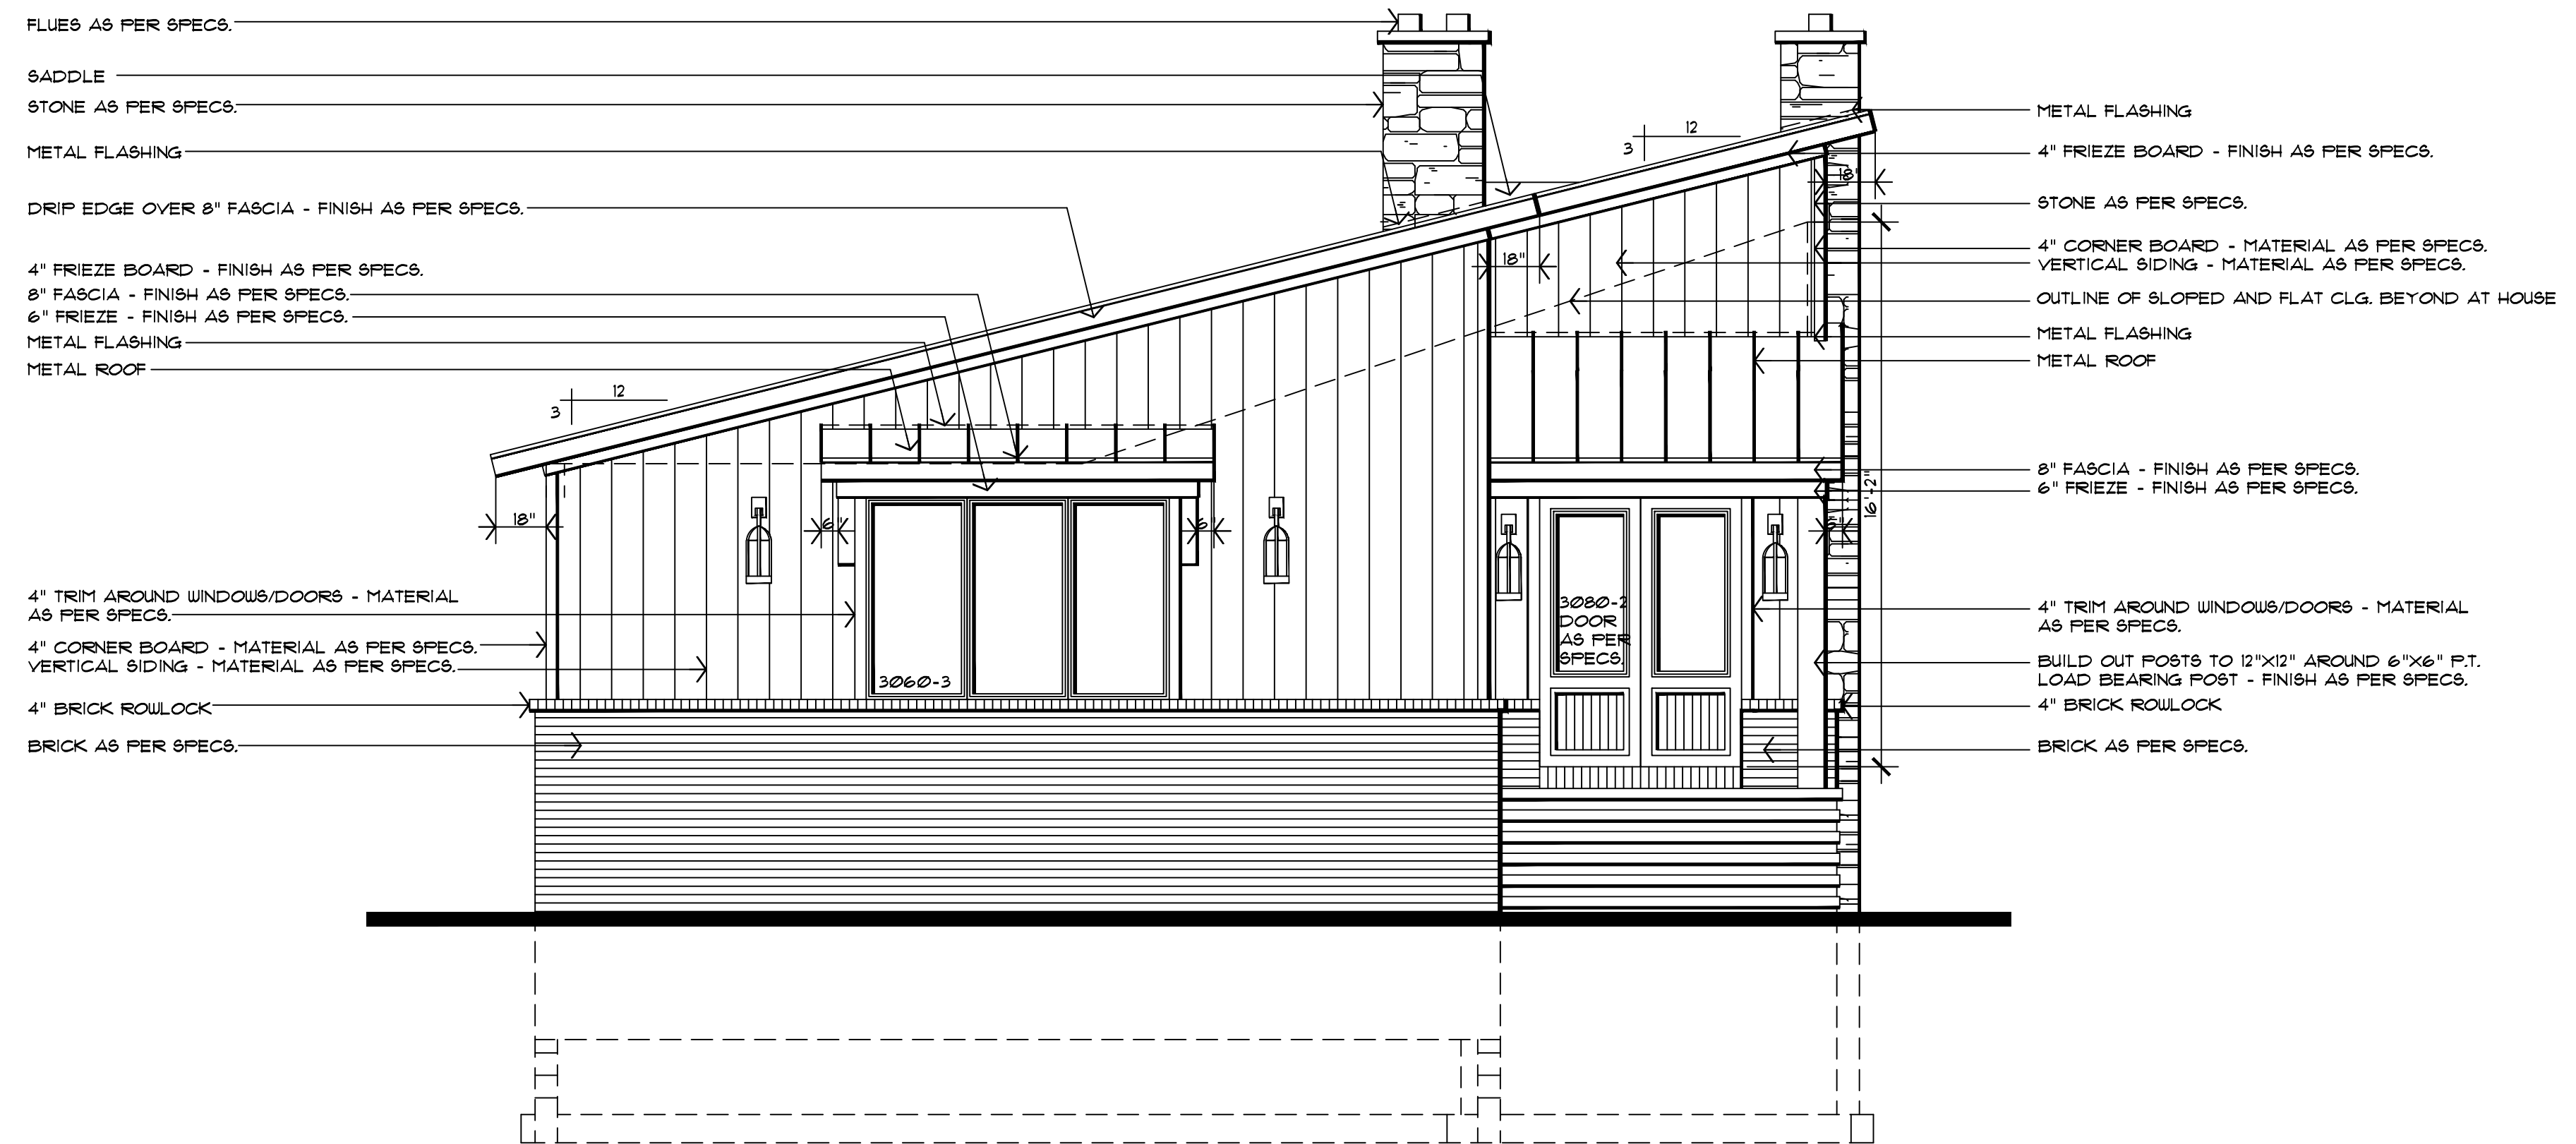

LAKESIDE (FRONT) ELEVATION

SCALE: 1/4"=1'-0"



ROADSIDE (REAR) ELEVATION

SCALE: 1/4"=1'-0"

DRAWING DESCRIPTION

ELEVATIONS

JOB #: 25-0905

SHEET 6 OF 7

REVISIONS

DRAWING DATES

☐ PRELIMINARY	DATE: 06/27/2025
☒ FINAL DRAWINGS	DATE: 09/05/2025
☐ PLOT PLAN	DATE:

HOME PLAN PREPARED FOR:

MATT DRESDEN

BUILDER:

Designed By:

Vild Design Group, Inc.

A Home Plan Design Company

Phone 248.755.6254

Email: VildDesignGroup@yahoo.com