


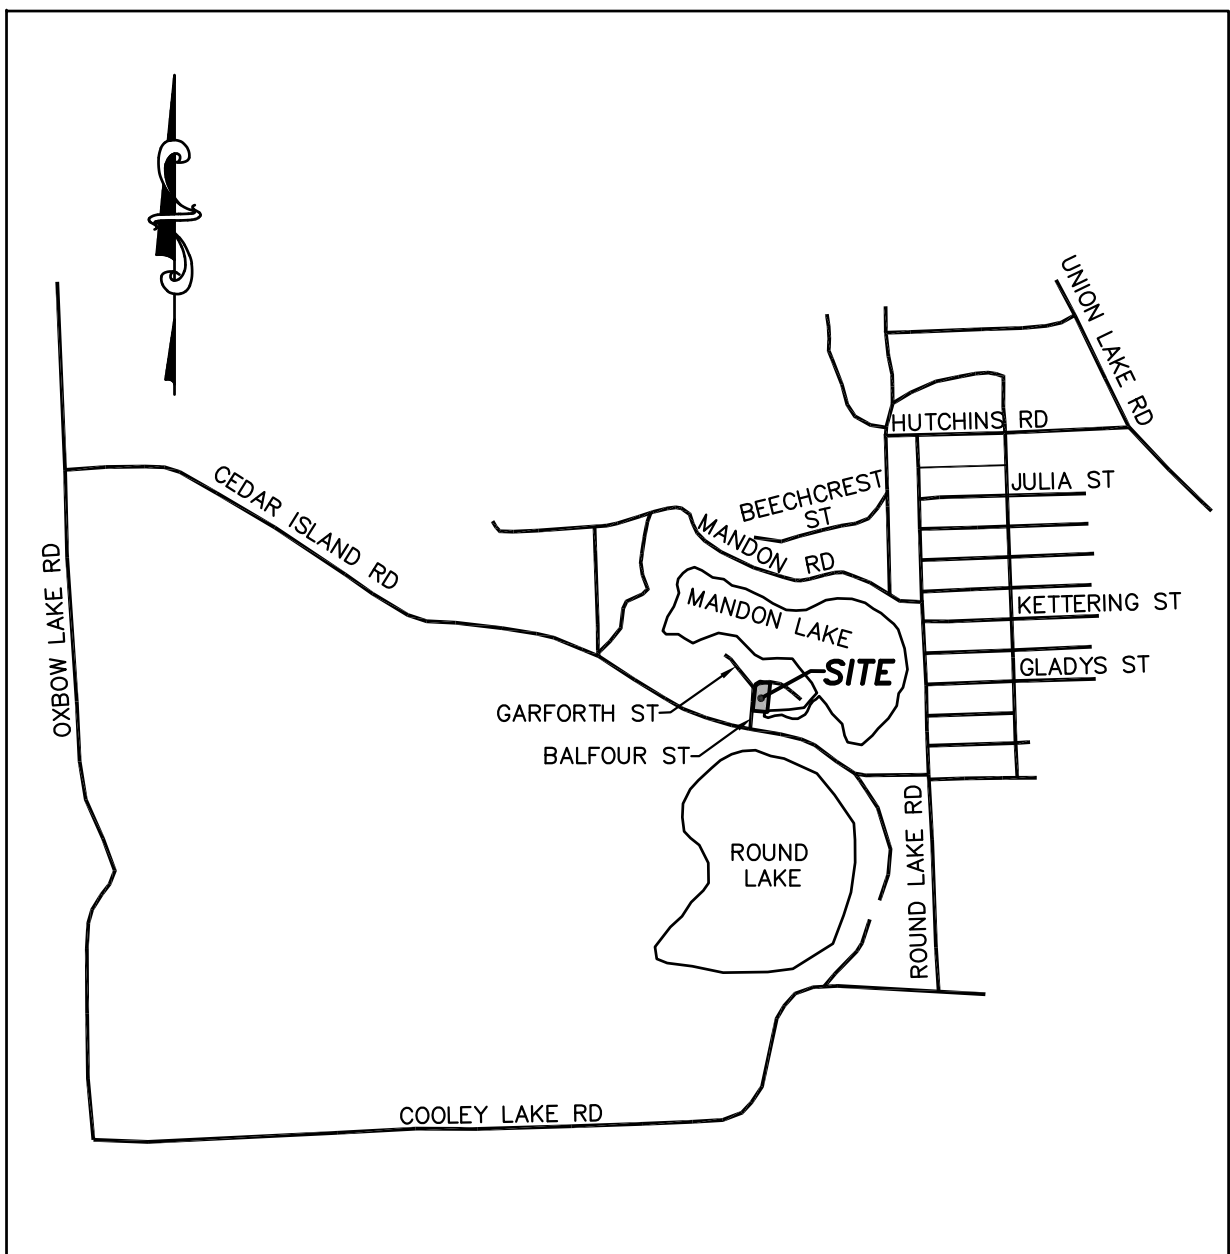

LOCATION MAP
NOT TO SCALE

LEGEND	
□ EX. CATCH BASIN	➤ EX. SATELLITE DISH
○ EX. MANHOLE	■ EX. SOIL BORING
▽ EX. END SECTION	⊙ EX. MONITOR WELL
⊕ EX. OVERFLOW STRUCTURE	⊙ FOUND IRON
⊙ EX. CLEANOUT	⊙ SET IRON
⊙ EX. HYDRANT	⊙ EX. BOULDER
⊙ EX. WATER SHUTOFF	⊙ EX. TREE STUMP
⊙ EX. FIRE DEPT. CONNECTION	⊙ EX. TREE
⊙ EX. WATER WELL	⊙ EX. TREE TAG & NUMBER
⊙ EX. LIGHTPOLE	— EX. TREE LINE
⊙ EX. UTILITY POLE	— EX. FENCE
⊙ EX. GUY ANCHOR	— EX. SANITARY SEWER
⊙ EX. TRAFFIC SIGNAL	— EX. STORM SEWER
⊙ EX. GAS SHUTOFF	— EX. WATER MAIN
⊙ EX. GAS VENT	— EX. ELECTRIC CABLE
⊙ EX. HANDHOLE	— EX. COMMUNICATION
⊙ EX. PEDESTAL	— EX. GAS LINE
⊙ EX. TRANSFORMER	— EX. OVERHEAD LINE
⊙ EX. GENERATOR	— PRO. SANITARY
⊙ EX. GAS METER	— PRO. STORM SEWER
⊙ EX. ELECTRIC METER	— PRO. WATER MAIN
⊙ EX. UTILITY MARKER	— PRO. SILT FENCE
⊙ EX. AIR CONDITIONER	— BENCHMARK
⊙ EX. RAILROAD SIGNAL	— PRO. DRAINAGE ARROW
⊙ EX. SIGN	— PRO. SPOT ELEVATION
⊙ EX. POST/BOLLARD	— PRO. DROP-BRICK LEDGE
⊙ EX. FLAGPOLE	— PRO. VIEW-OUT ELEVATION
⊙ EX. MAILBOX	— PRO. WALK-OUT ELEVATION
⊙ EX. PARKING METER	— TREE REMOVAL

DESCRIPTION:

T3N, R8E, SEC 35 ROUND LAKE OVERLOOK LOTS
1, 2, 16 & 17 BLK 2

ZONING:

R1-D SINGLE FAMILY RESIDENTIAL
SETBACKS: FRONT 30'
SIDES 10'
REAR 30'

NOTICE:

CONSTRUCTION SITE SAFETY IS THE SOLE RESPONSIBILITY OF THE CONTRACTOR NEITHER THE OWNER NOR THE ENGINEER SHALL BE EXPECTED TO ASSUME ANY RESPONSIBILITY FOR SAFETY OF THE WORK, OF PERSONS ENGAGED IN THE WORK, OF ANY NEARBY STRUCTURES, OR OF ANY OTHER PERSONS.

NOTE:


THE LOCATIONS OF EXISTING UNDERGROUND UTILITIES ARE SHOWN IN AN APPROXIMATE WAY ONLY AS DISCLOSED BY AVAILABLE UTILITY COMPANY RECORDS AND HAVE NOT BEEN INDEPENDENTLY VERIFIED BY THE COMPANY. NO GUARANTEE IS EITHER EXPRESSED OR IMPLIED AS TO THE COMPLETENESS OR ACCURACY THEREOF. THE CONTRACTOR SHALL DETERMINE THE EXACT LOCATION OF ALL EXISTING UTILITIES BEFORE COMMENCING WORK, AND AGREES TO BE FULLY RESPONSIBLE FOR ANY AND ALL DAMAGES WHICH MIGHT BE OCCASIONED BY THE CONTRACTOR'S FAILURE TO EXACTLY LOCATE AND PRESERVE ANY AND ALL UNDERGROUND UTILITIES. THE CONTRACTOR SHALL NOTIFY THE DESIGN ENGINEER IMMEDIATELY IF A CONFLICT IS APPARENT.

NOTES:

- 1.) BEARINGS BASED ON MICHIGAN STATE PLANE COORDINATES, NAD83, MICHIGAN SOUTH ZONE
- 2.) TITLE WORK NOT PROVIDED.
- 3.) DRAINAGE ON THIS PROPERTY CANNOT AFFECT ADJACENT PROPERTIES.
- 4.) MAINTAIN POSITIVE DRAINAGE ON SITE AND AWAY FROM PROPOSED STRUCTURES.
- 5.) A SEC PERMIT WILL BE REQUIRED FROM OCWR.
- 6.) DEFER TO RCOC FOR RIGHT OF WAY PERMIT/WORK REQUIREMENTS.

BENCHMARK:


SPIKE IN NORTH SIDE 15" ELM APPROXIMATELY 90 FEET NORTH OF THE SOUTHWEST PROPERTY CORNER, ELEVATION 942.20 NAVD88

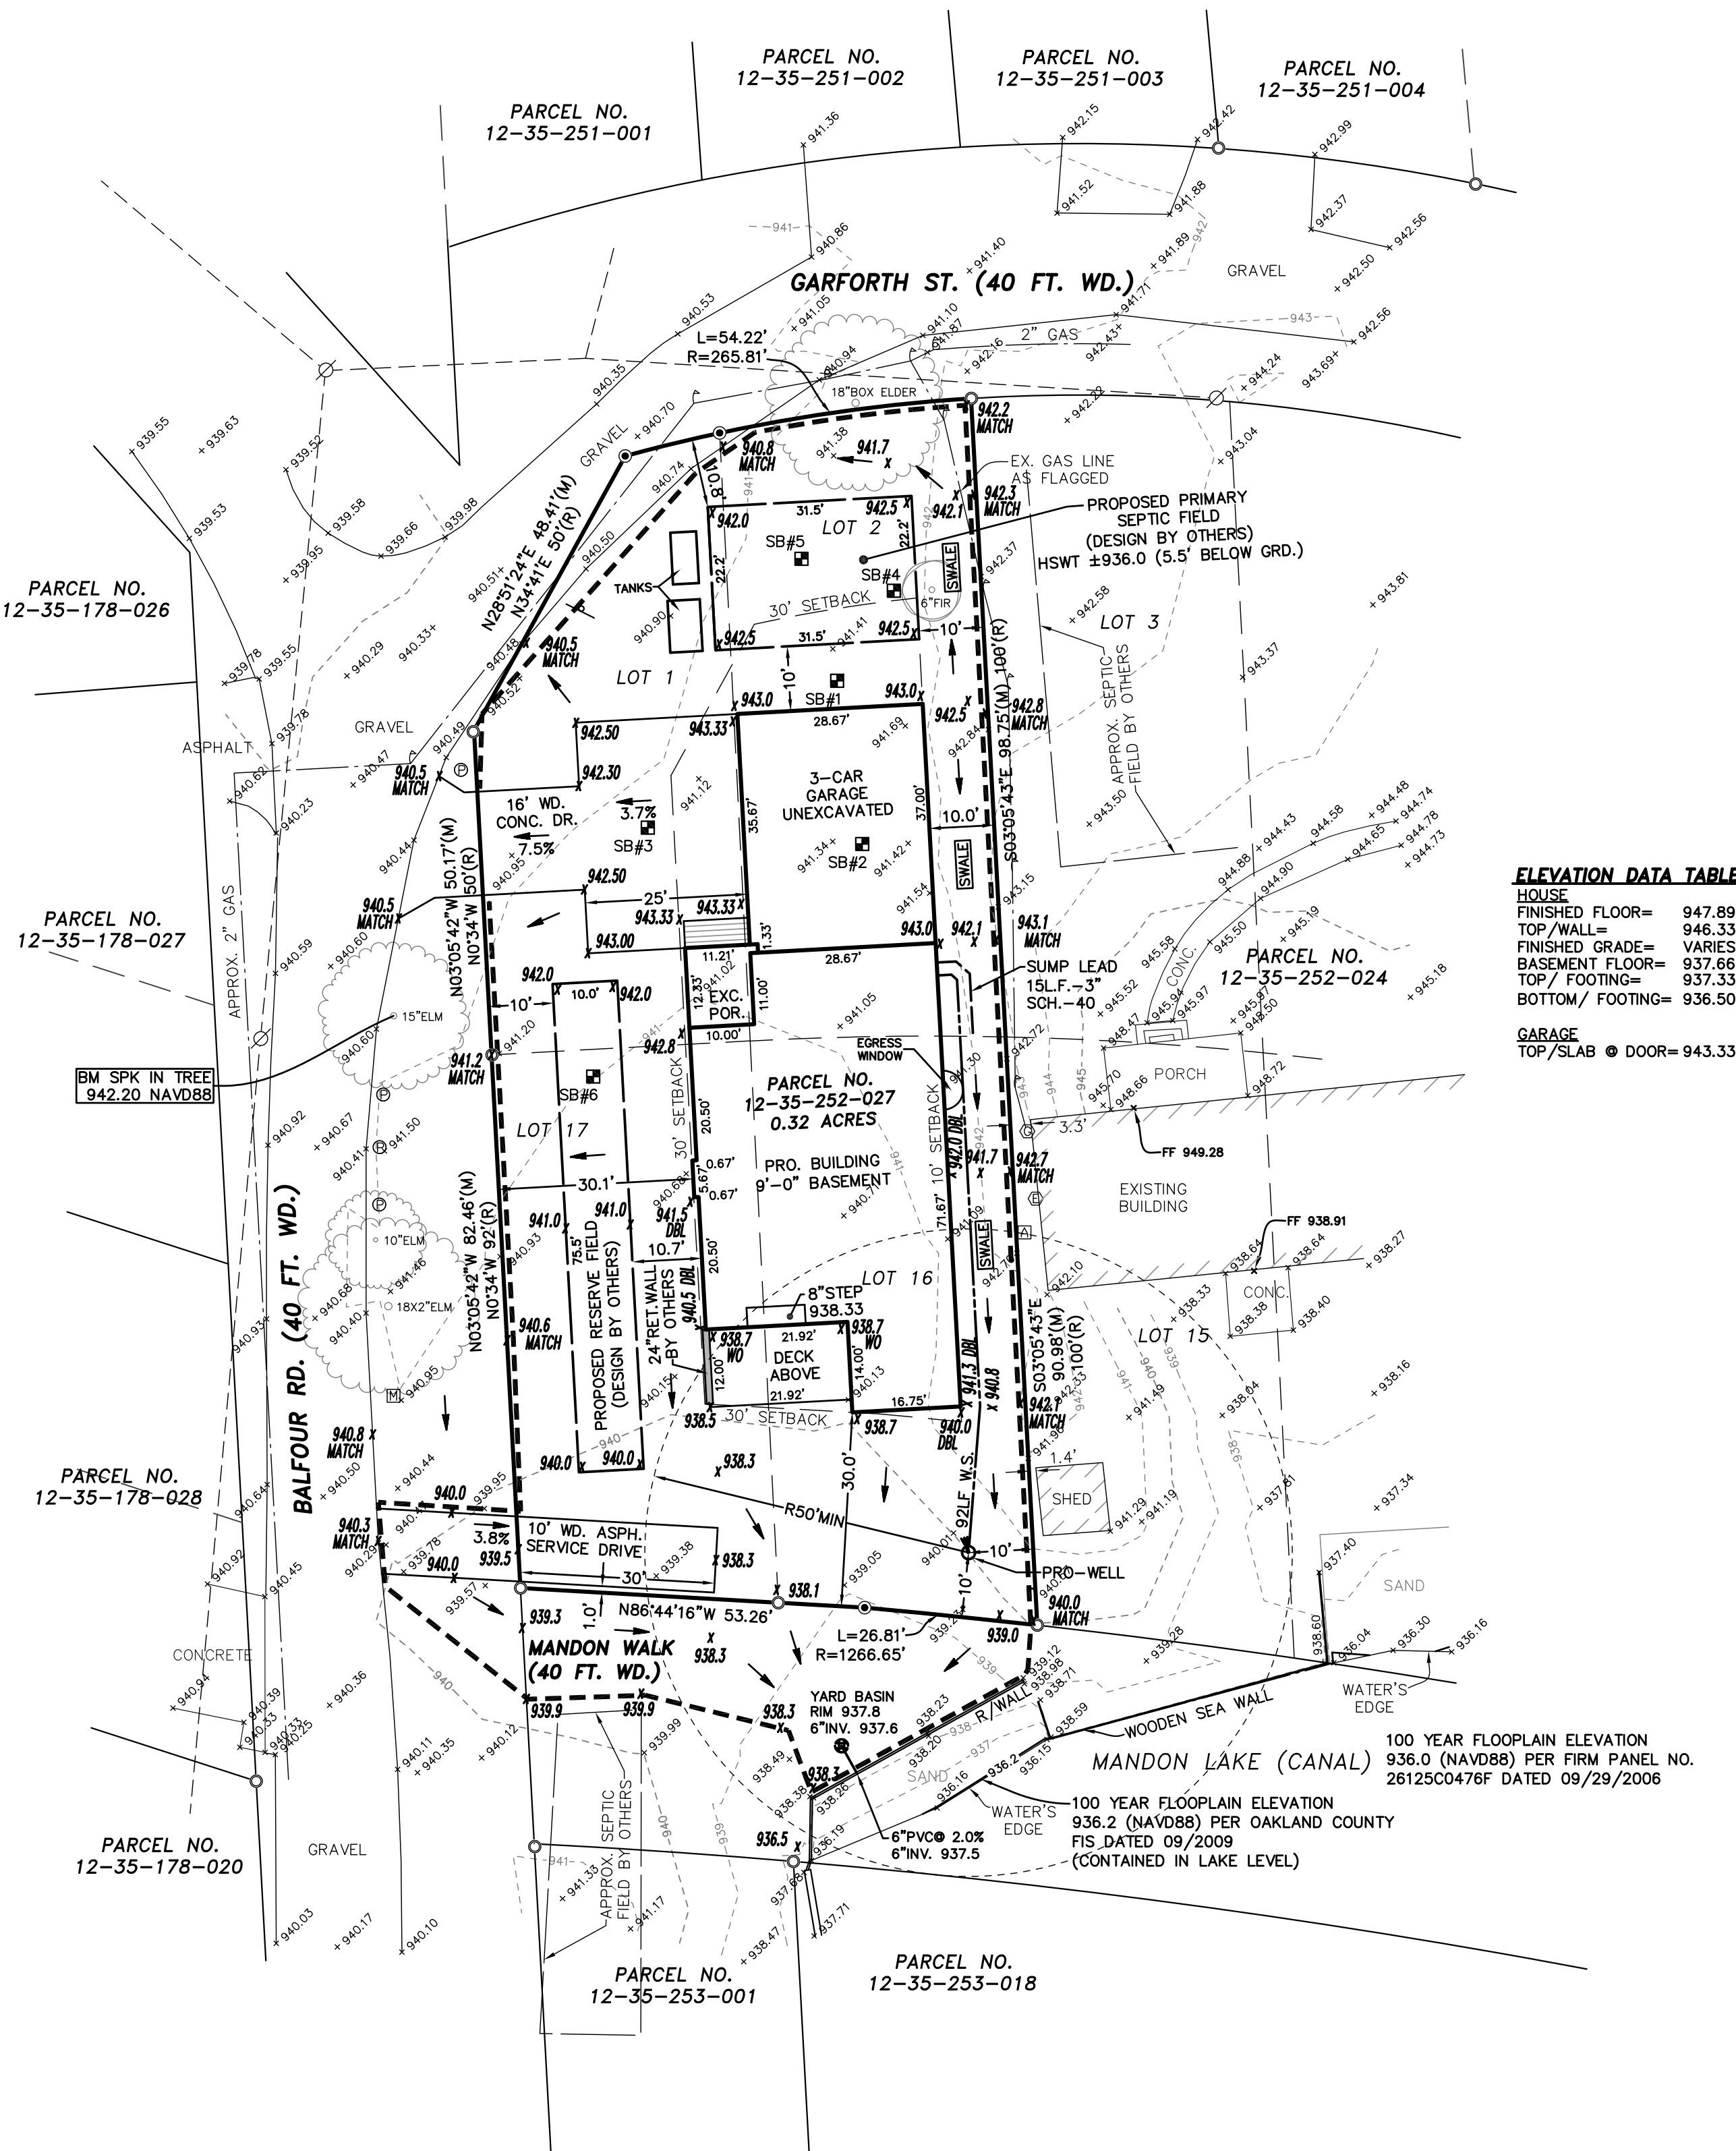

ELEVATION DATA TABLE:

HOUSE
FINISHED FLOOR= 947.89
TOP/WALL= 946.33
FINISHED GRADE= VARIES
BASEMENT FLOOR= 937.66
TOP/ FOOTING= 937.33
BOTTOM/ FOOTING= 936.50

GARAGE
TOP/SLAB @ DOOR= 943.33

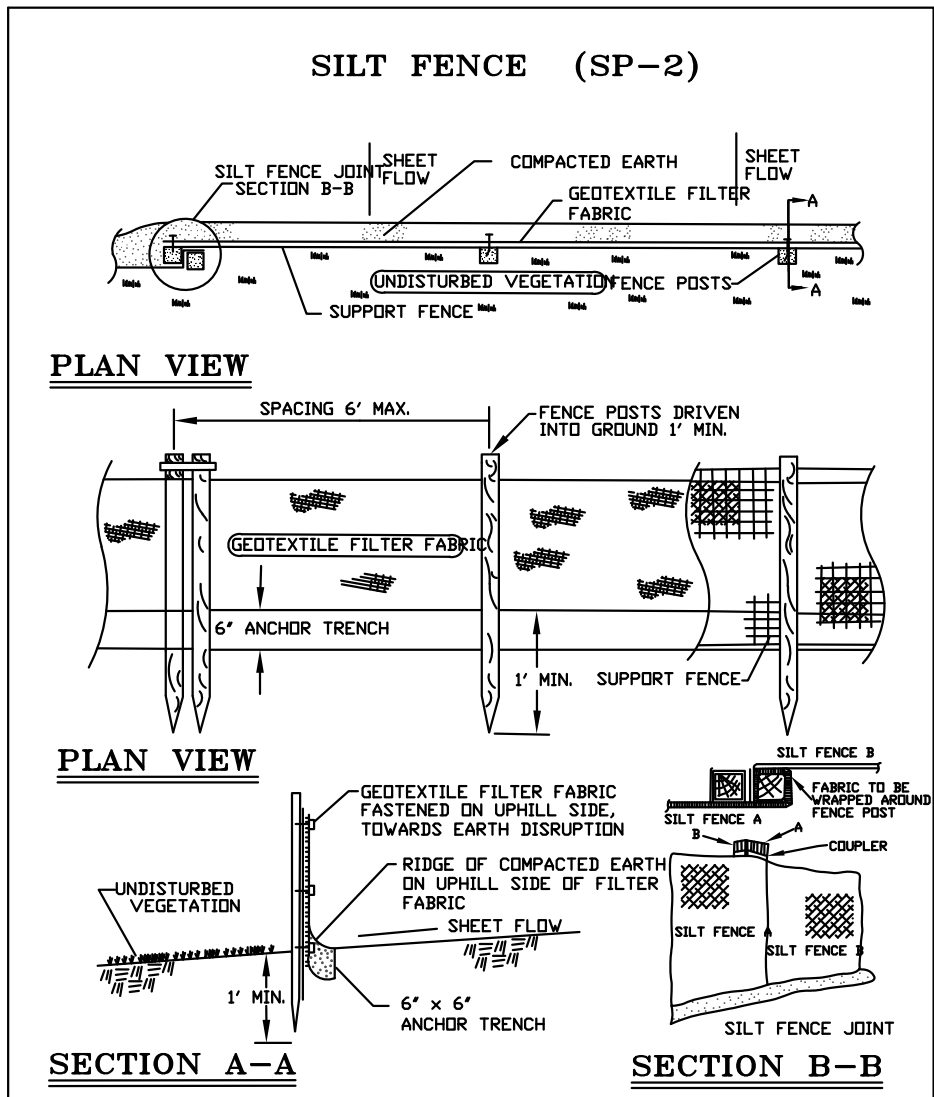

CLIENT: MATTHEW DRESDEN-1881 REIDSVIEW DR. WHITE LAKE, MI 48383

(248) 943-7335

PLOT PLAN

PARCEL NO. 12-35-252-027
SECTION: 35
TOWNSHIP: 3N
WHITE LAKE TOWNSHIP
OAKLAND COUNTY
MICHIGAN
RANGE: 8E

REVISED

DATE: 10/23/2025

DRAWN BY: TTP

CHECKED BY: KEH

FBK: 447

CHF: BK

SCALE: HOR 1"=20 FT.
VER 1"=20 FT.


1

25-238

COMMERCIAL
SITE PLANNING
SITE ENGINEERING
INDUSTRIAL & MULTI-UNIT
LAND SURVEYING
CONSTRUCTION LAYOUT

SURVEYING
ALTA SURVEYS
BOUNDARY SURVEYS
TOPOGRAPHIC SURVEYS
PARCEL SPLITS

RESIDENTIAL
SUBDIVISIONS
SITE CONDOMINIUM
MULTI-FAMILY
SPLIT PLANS
CONSTRUCTION LAYOUT

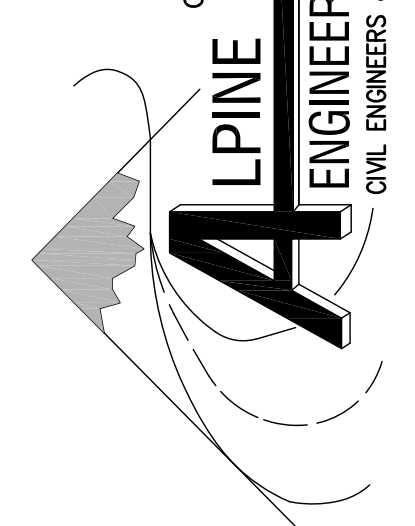

811
Know what's below
Call before you dig.