


NOTE:

BEARINGS BASED ON MICHIGAN
STATE PLANE COORDINATES,
NAD83, MICHIGAN SOUTH ZONE

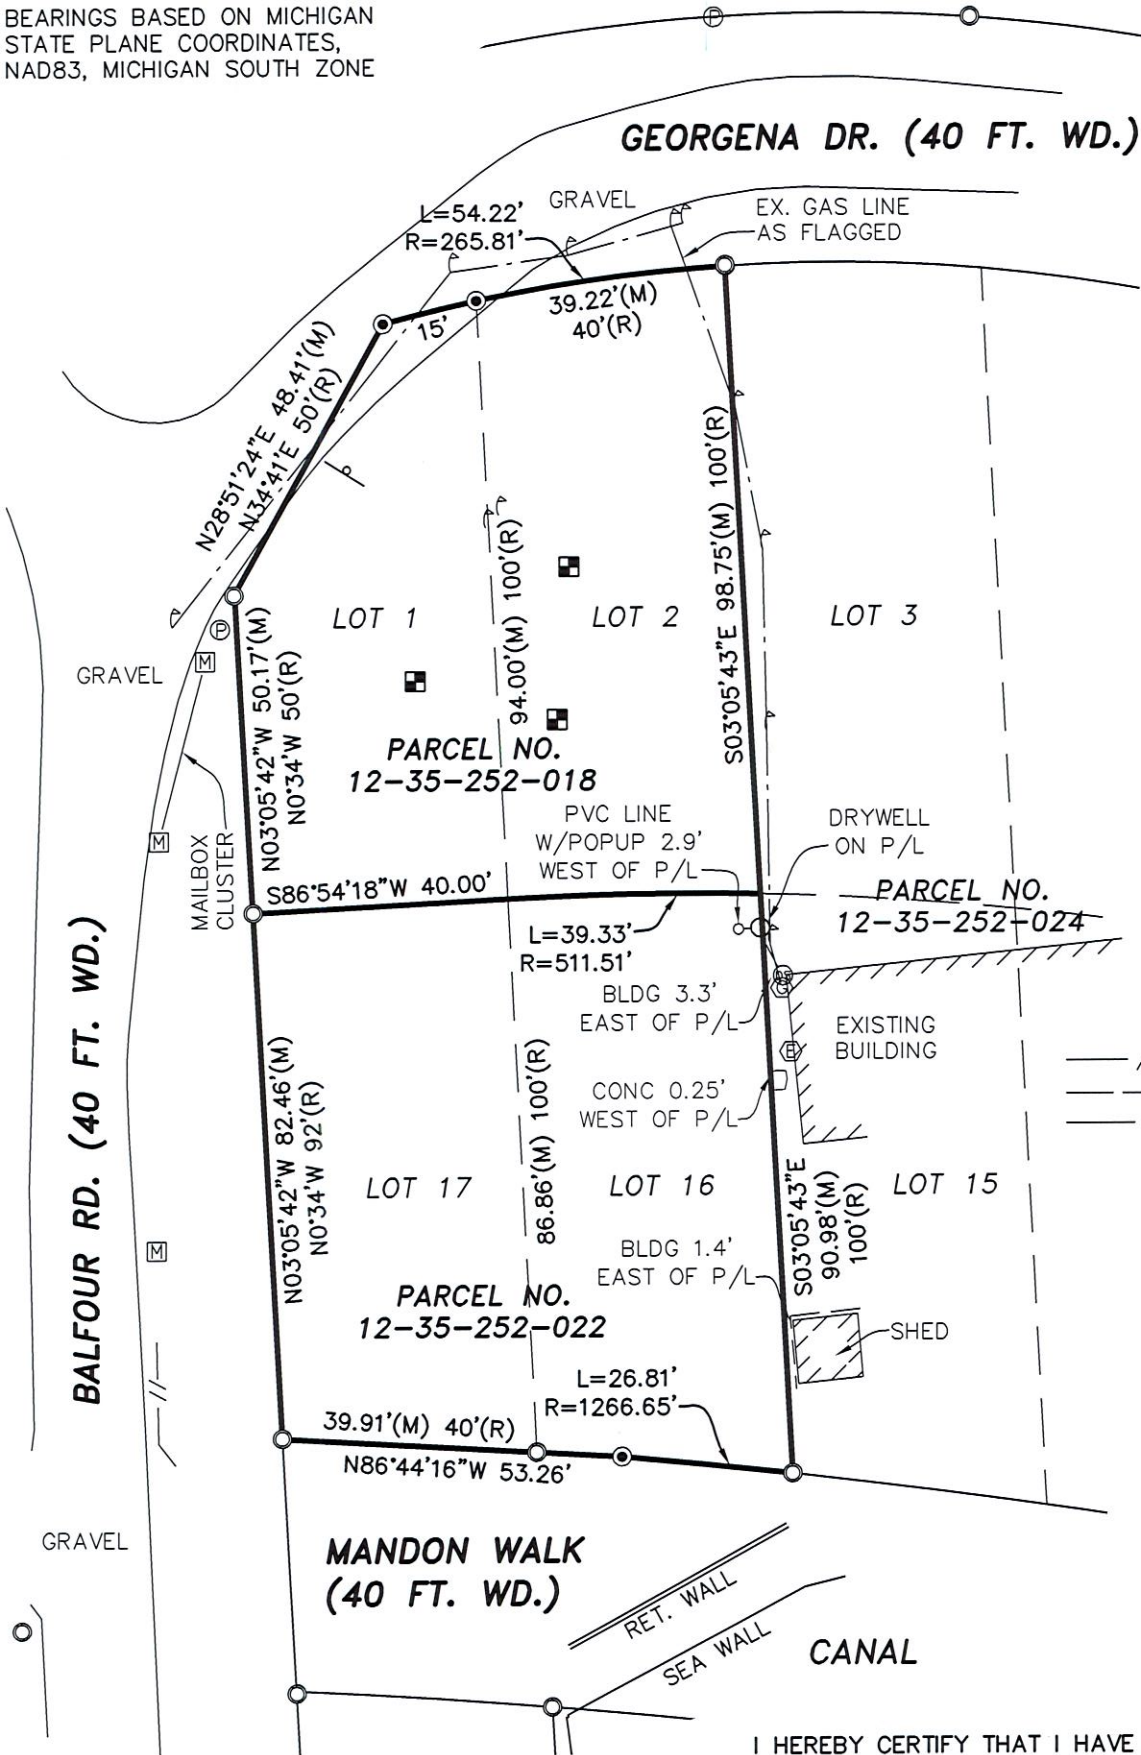

LEGEND

- EX. MANHOLE
- △ EX. END SECTION
- ⊙ EX. DOWNSPOUT
- ⊙ EX. CLEANOUT
- ⊙ EX. GAS METER
- ⊙ EX. ELECTRIC METER
- ↑ EX. UTILITY MARKER
- ⊠ EX. HVAC
- EX. SIGN
- ⊙ EX. POST/BOLLARD
- ⊠ EX. MAILBOX
- ⊠ EX. SOIL BORING
- FOUND IRON
- ⊙ SET IRON
- // — EX. FENCE
- — — EX. STORM SEWER
- · — EX. GAS LINE



DESCRIPTIONS:

PARCEL NO. 12-35-252-018:
T3N, R8E, SEC 35 ROUND LAKE OVERLOOK
LOTS 1 & 2 BLK 2
PARCEL NO. 12-35-252-022:
T3N, R8E, SEC 35 ROUND LAKE OVERLOOK
LOTS 16 & 17 BLK 2

I HEREBY CERTIFY THAT I HAVE SURVEYED THE PROPERTY
HEREIN DESCRIBED, AND THAT THERE ARE NO VISIBLE
ENCROACHMENTS UPON THE ABOVE DESCRIBED PROPERTY,
EXCEPT AS SHOWN HEREON. I CERTIFY THAT THE
REQUIREMENTS FOR 1970 PA 132, MCL 54.213 HAVE BEEN
MET. THE RELATIVE POSITIONAL PRECISION OF THE
CORNERS IDENTIFIED FOR THIS SURVEY AND SHOWN ON
THE MAP ARE WITHIN THE LIMITS ACCEPTED BY THE
PRACTICE OF PROFESSIONAL SURVEYING.

Kenneth E. Hindle
KENNETH E. HINDLE
PROFESSIONAL SURVEYOR NO. 4001054053

ALPINE
ENGINEERING, INC.
CIVIL ENGINEERS & LAND SURVEYORS
46892 WEST ROAD
SUITE 109
NOVI, MICHIGAN 48377
(248) 926-3701 (BUS)
(248) 926-3765 (FAX)

CLIENT: NANCY C. REISTER, KAREN S. CAMPBELL & MATTHEW DRESDEN BOUNDARY SURVEY 12-35-252-018 & 12-35-252-022 SECTION: 35 TOWNSHIP: 3N RANGE: 8E WHITE LAKE TOWNSHIP OAKLAND COUNTY MICHIGAN	DATE: 4-3-25
	DRAWN BY: GP
	CHECKED BY: KEH
	SCALE HOR 1"= 30 FT. VER 1"= - FT.
FBK: 432	
CHF: RDF	
0 15 30	
1	
25-238	