


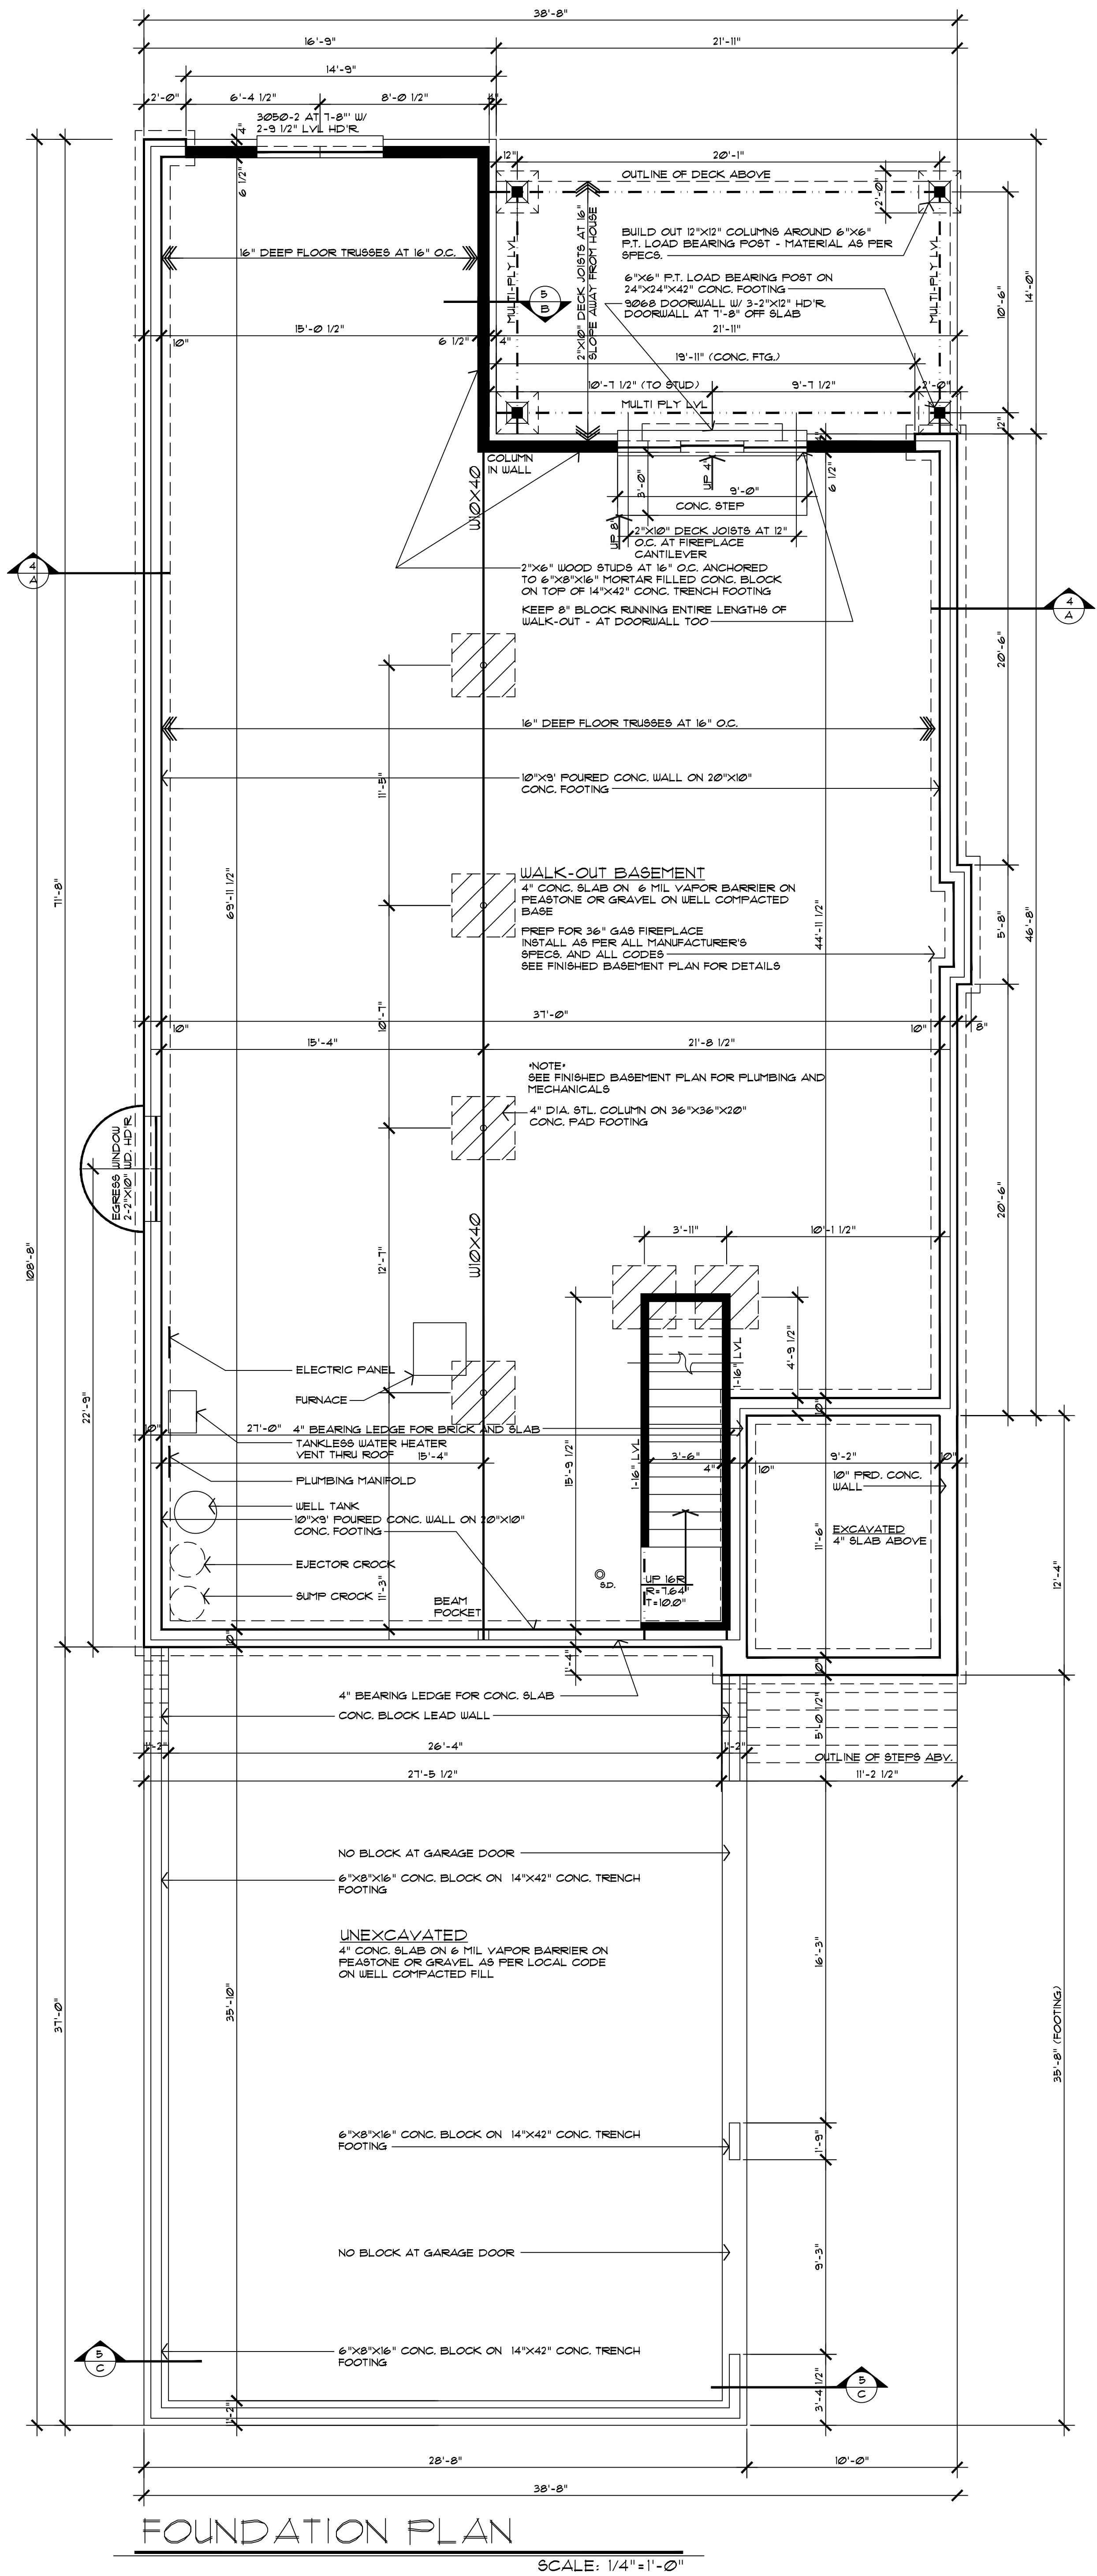

FOUNDATION PLAN

SCALE: 1/4"=1'-0"

Designed By:

Vild Design Group, Inc.

A Home Plan Design Company
Phone 248.755.6254
Email: VildDesignGroup@yahoo.com

HOME PLAN PREPARED FOR:
MATT DRESDEN

BUILDER:

DRAWING DATES

- ☐ PRELIMINARY
DATE: 06/27/2025
- ☒ FINAL DRAWINGS
DATE: 09/05/2025
- ☐ PLOT PLAN
DATE:

REVISIONS

DRAWING DESCRIPTION

- FOUNDATION PLAN
-
- JOB #: 25-0905
- SHEET 1 OF 1