


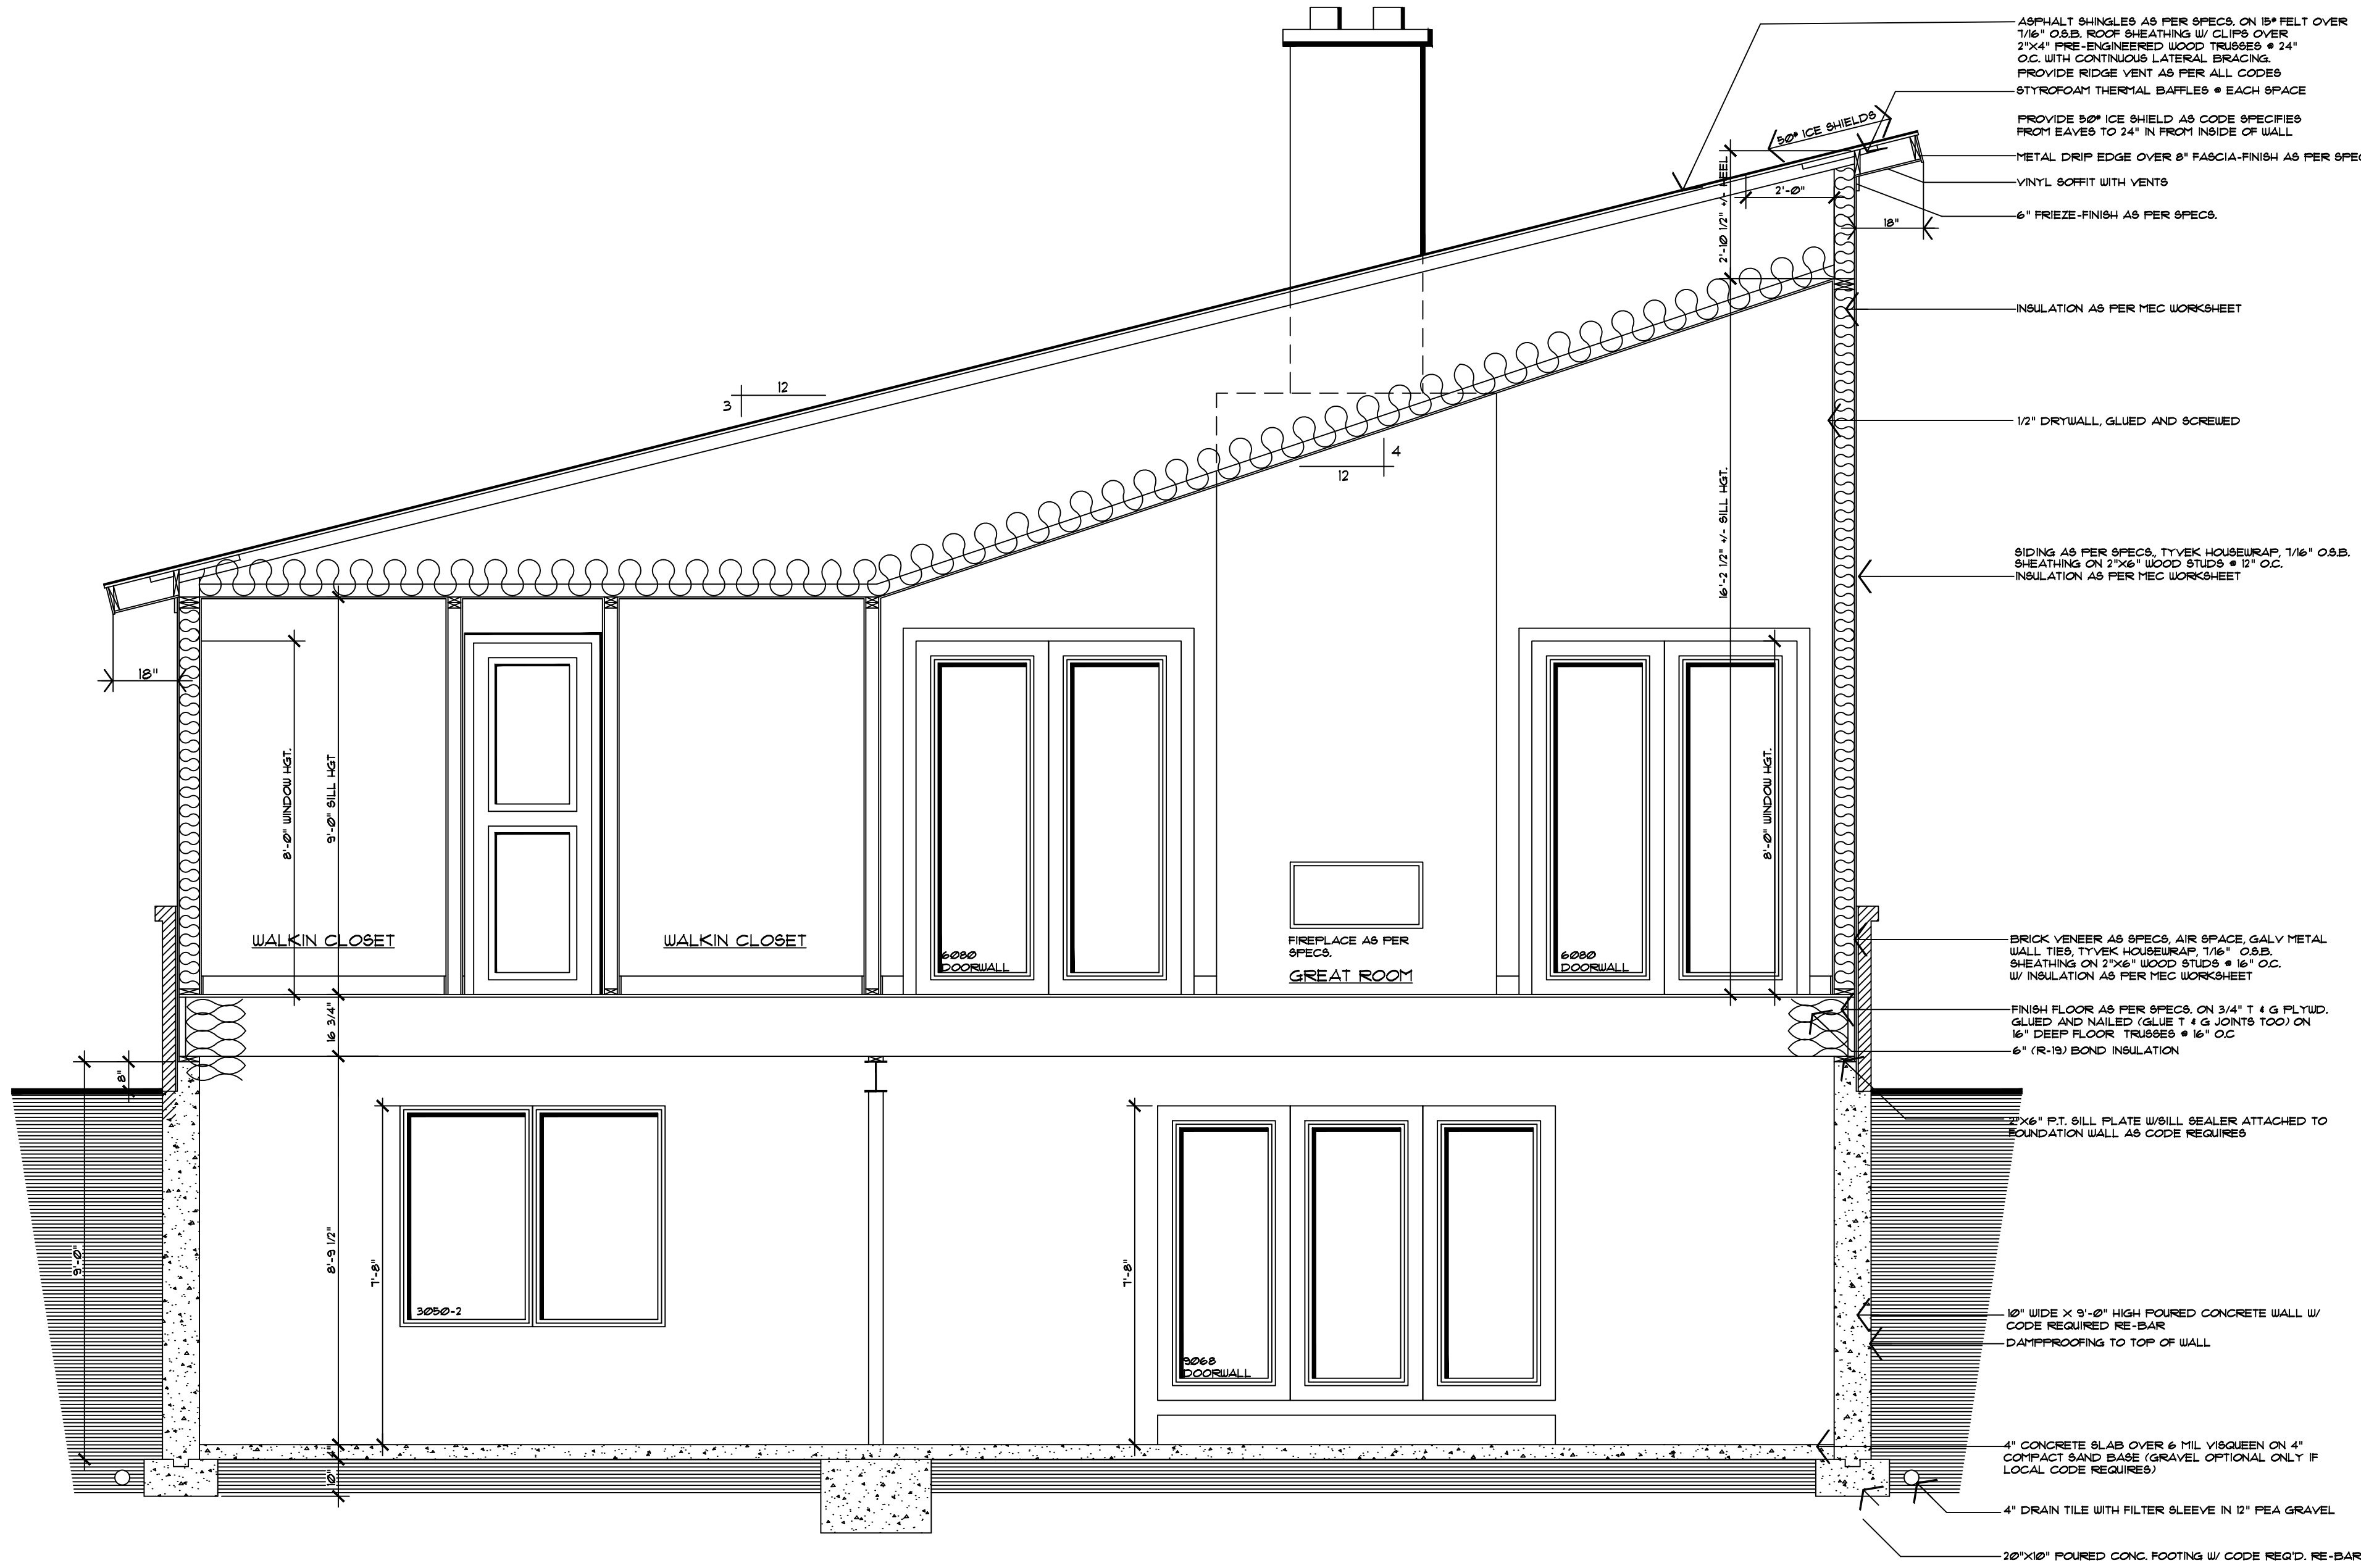

TRANSVERSE SECTION "4-A"

SCALE: 3/8"=1'-0"

Designed By:

Vild Design Group, Inc.
A Home Plan Design Company
Phone 248.755.6254
Email: VildDesignGroup@yahoo.com

HOME PLAN PREPARED FOR:
MATT DRESDEN

BUILDER:

DRAWING DATES

☐ PRELIMINARY
DATE: 06/27/2025
☒ FINAL DRAWINGS
DATE: 09/05/2025
☐ FLOT PLAN
DATE:

REVISIONS

DRAWING DESCRIPTION

SECTIONS

JOB #: 25-0905
SHEET 4 OF 7